




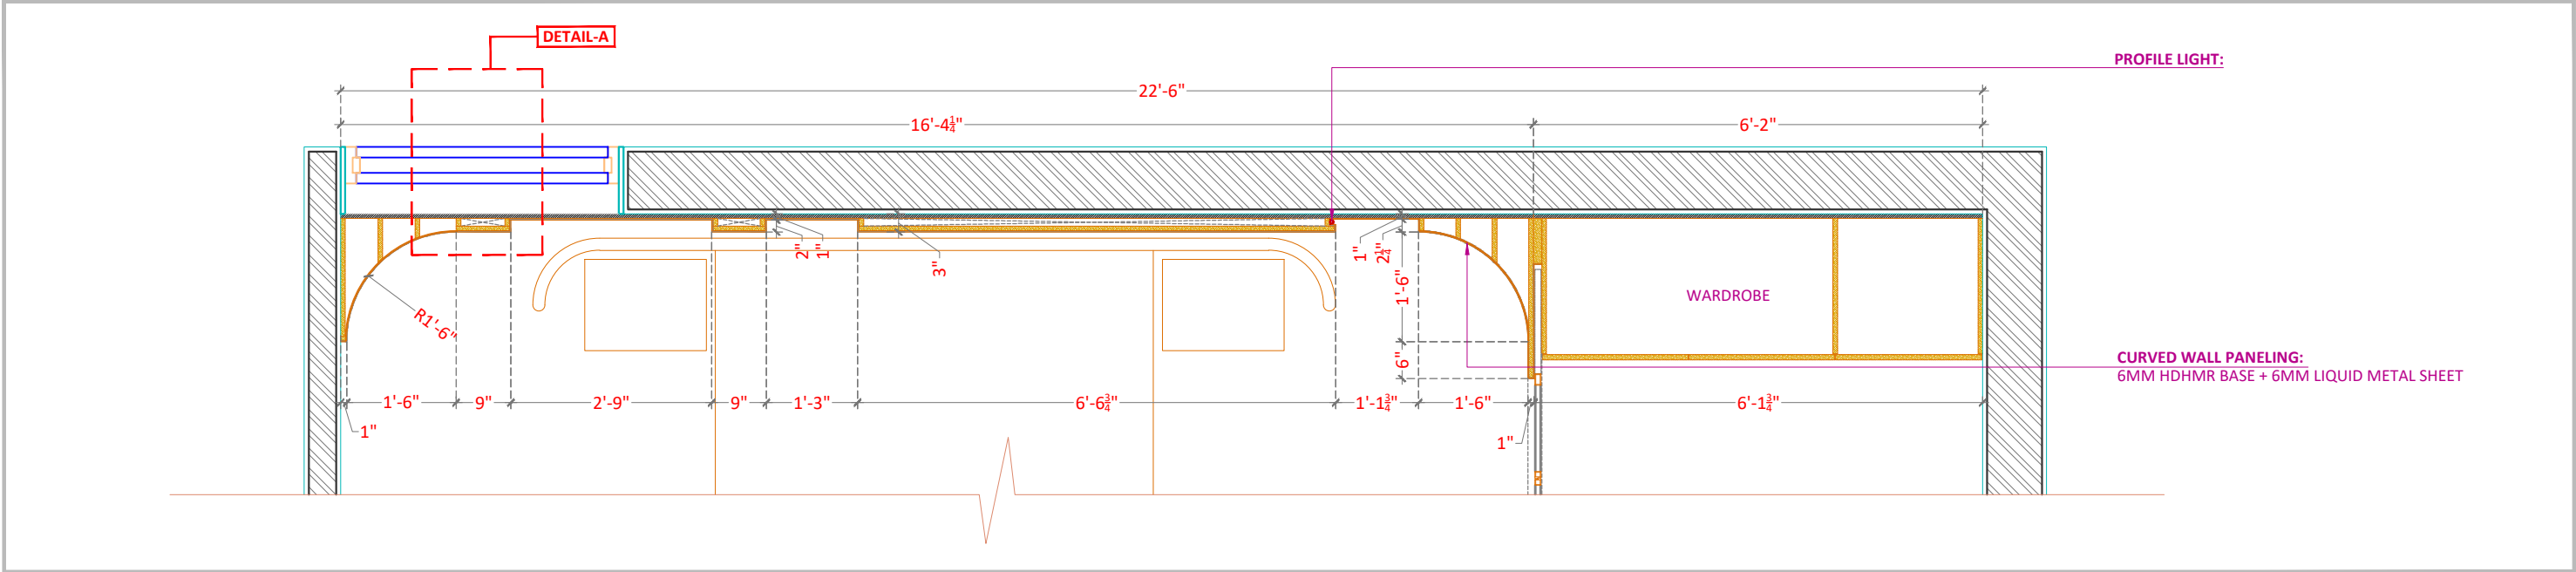


A)PART WORKING PLAN

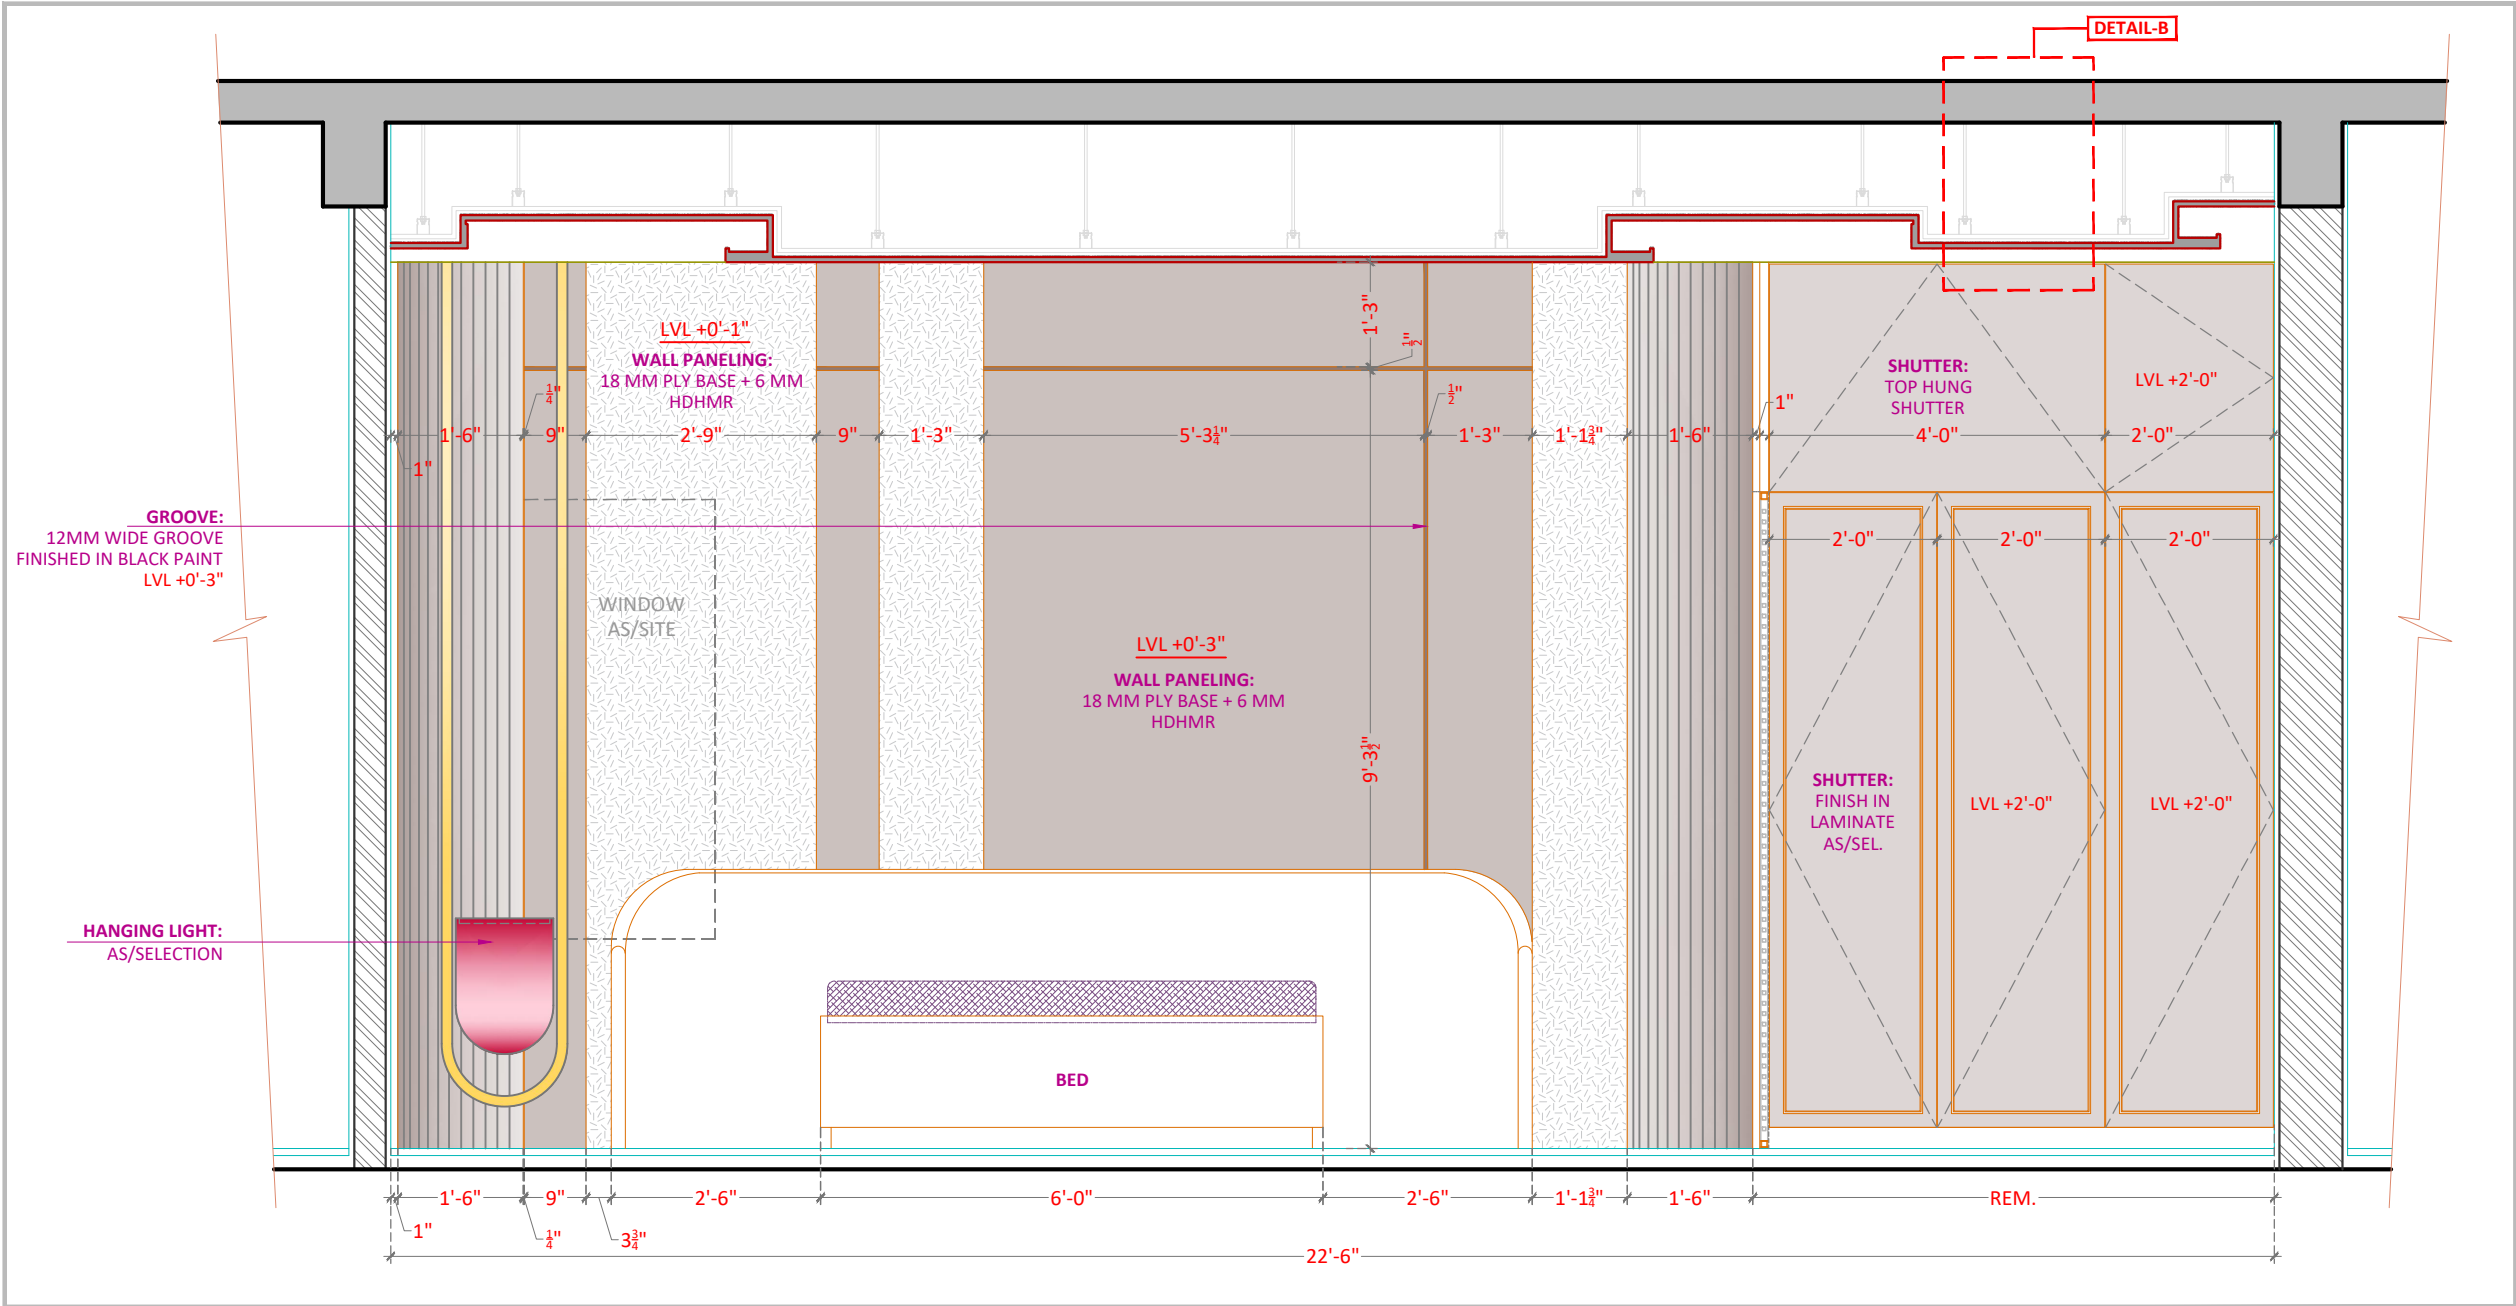

B)WORKING ELEVATION

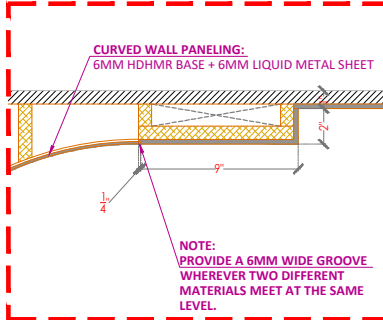

C)DETAIL-A

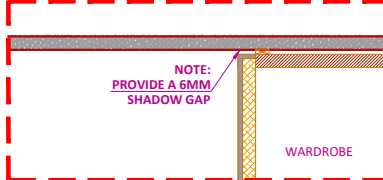

D)DETAIL-B

MASTER BEDROOM - BED BACK DETAIL