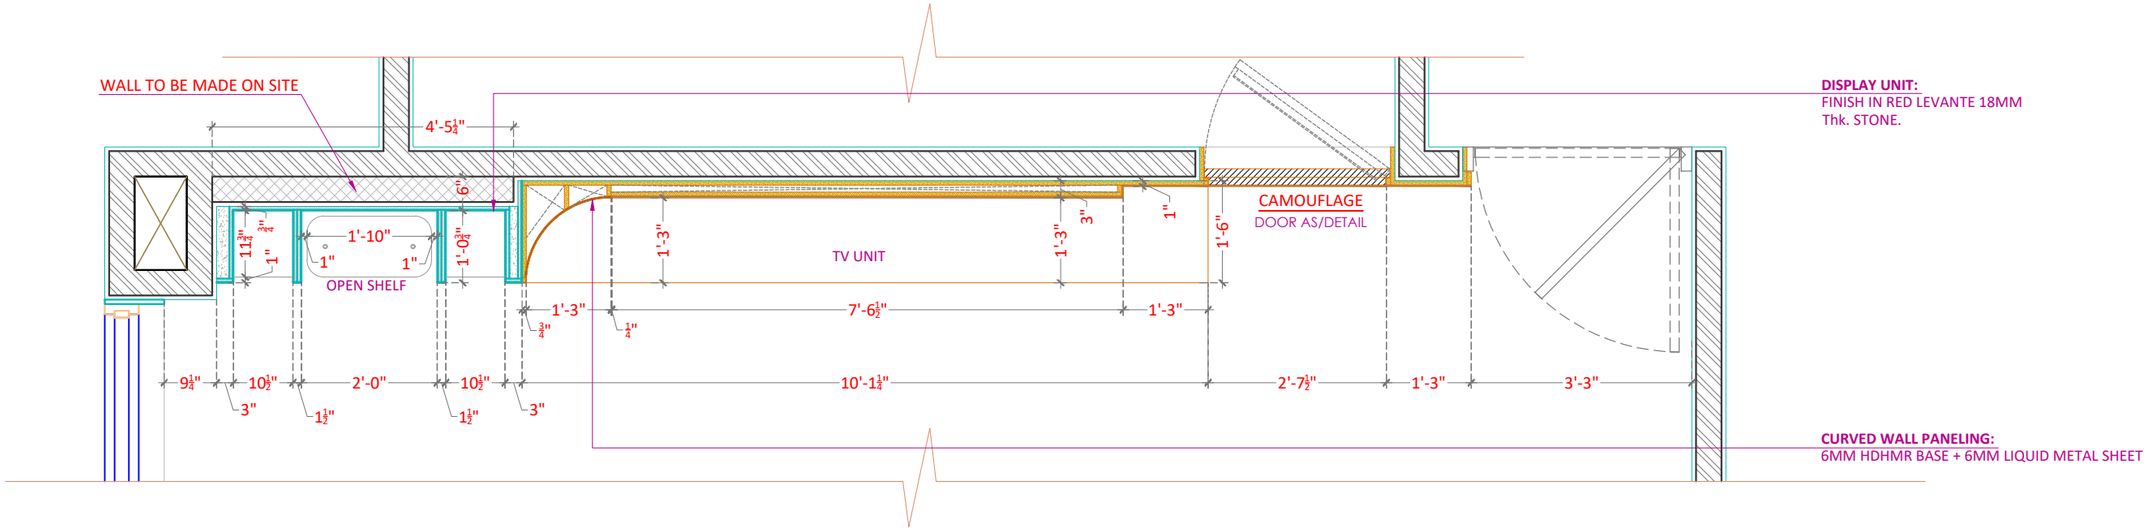

A)PART WORKING PLAN

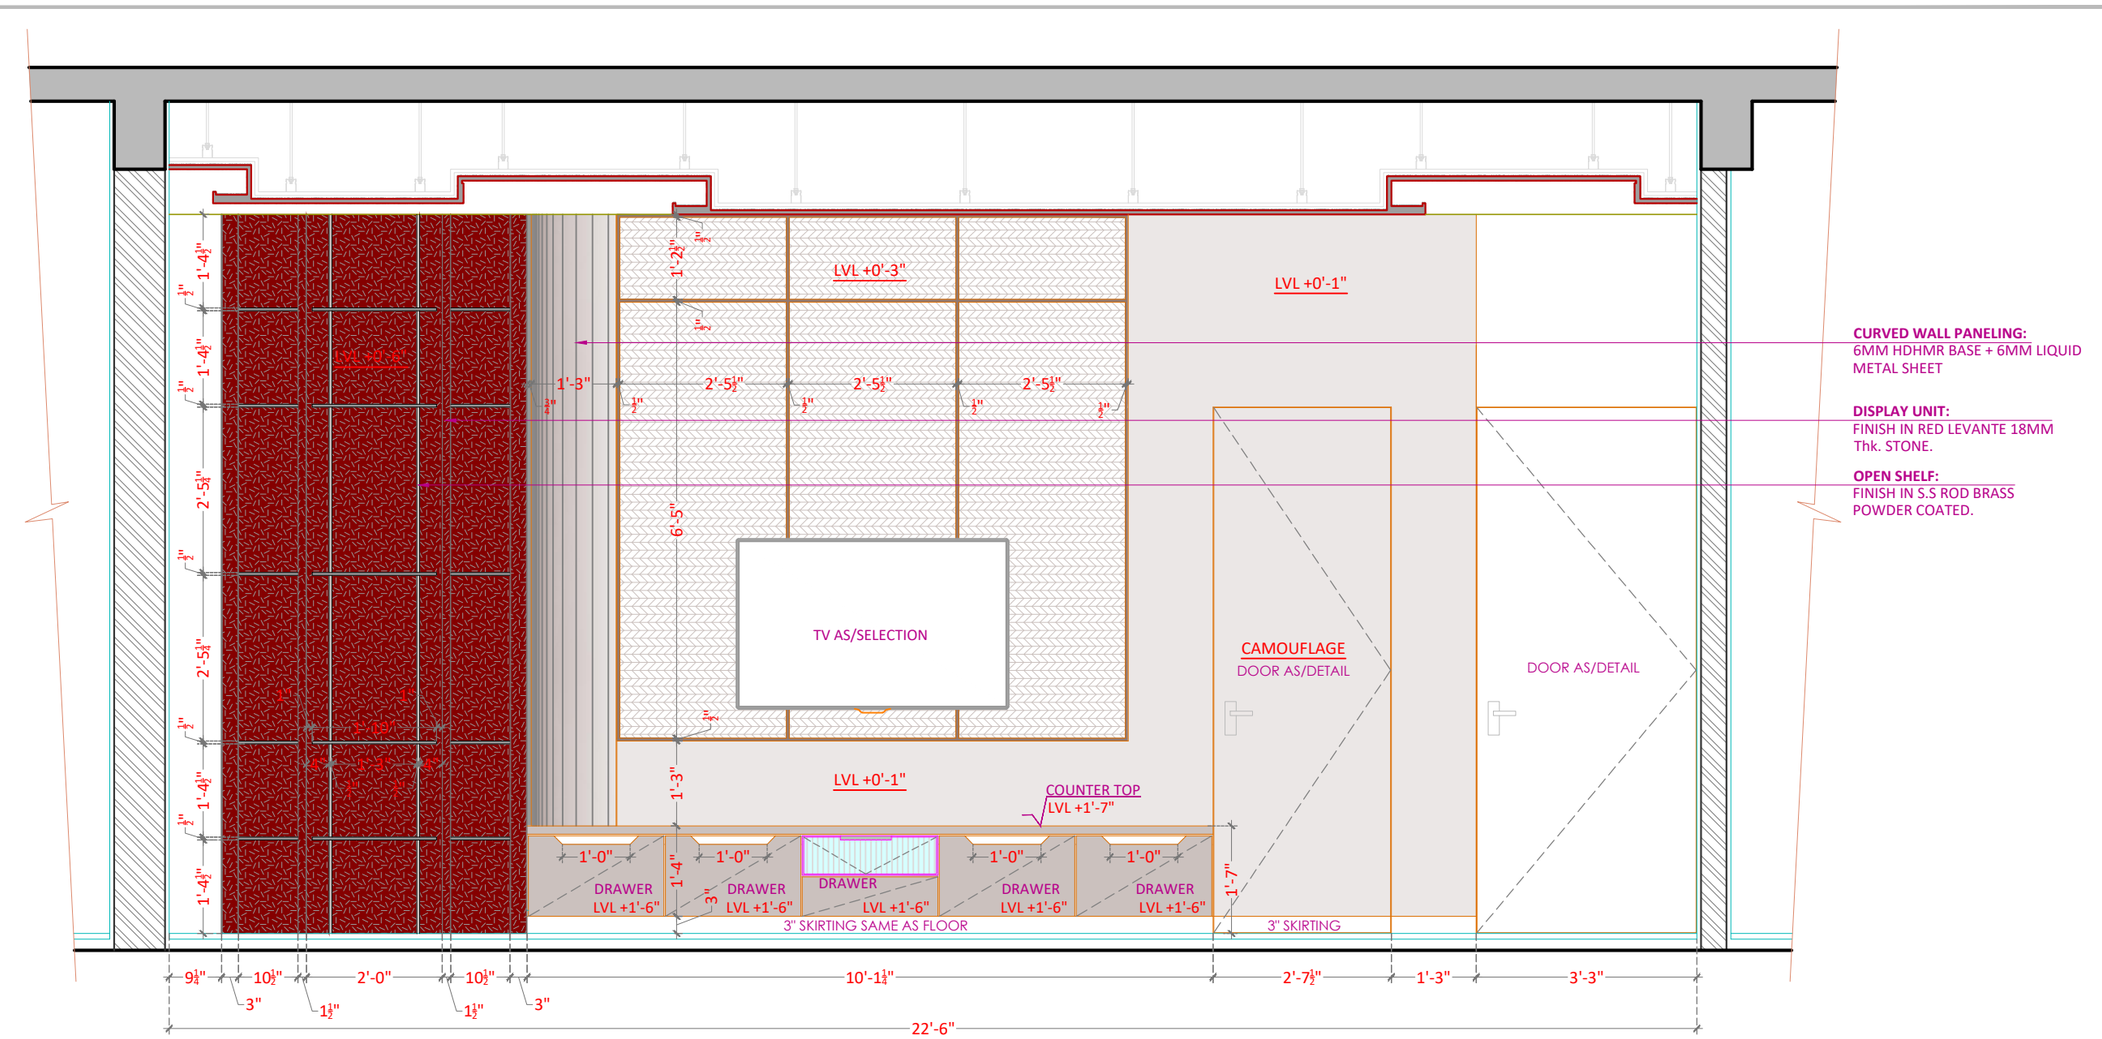

B)WORKING ELEVATION

MASTER BEDROOM - TV UNIT DETAIL