

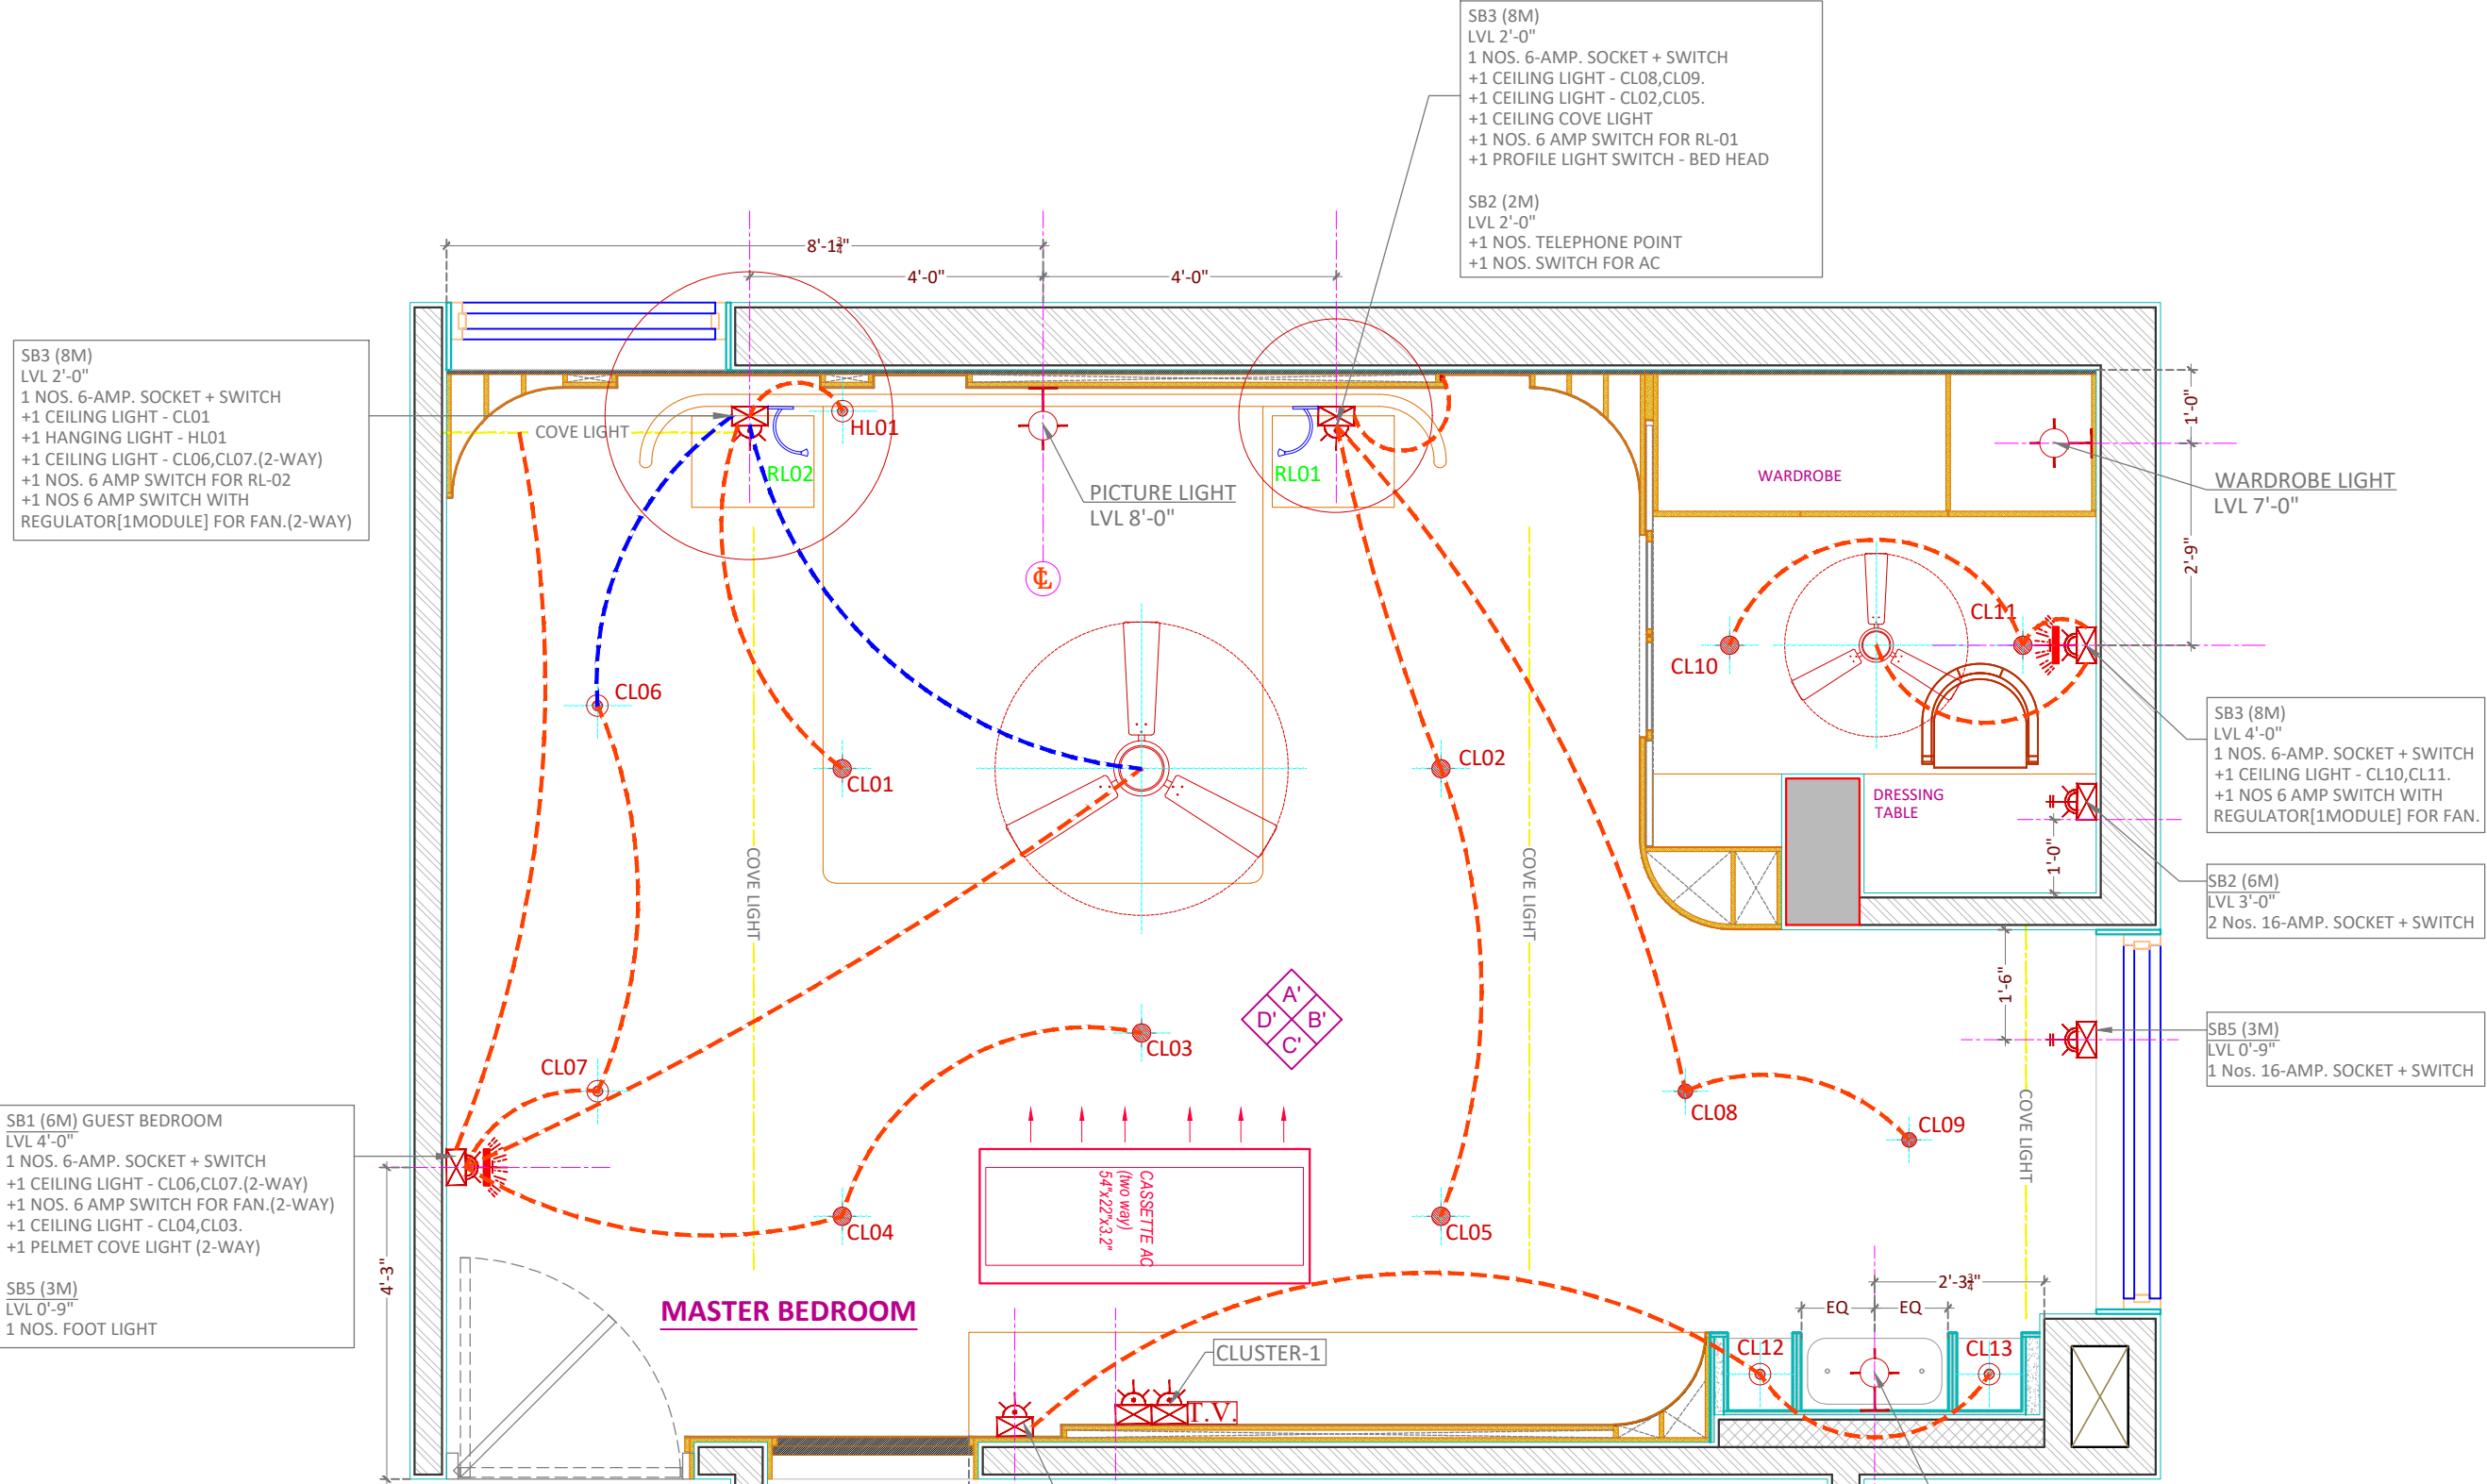


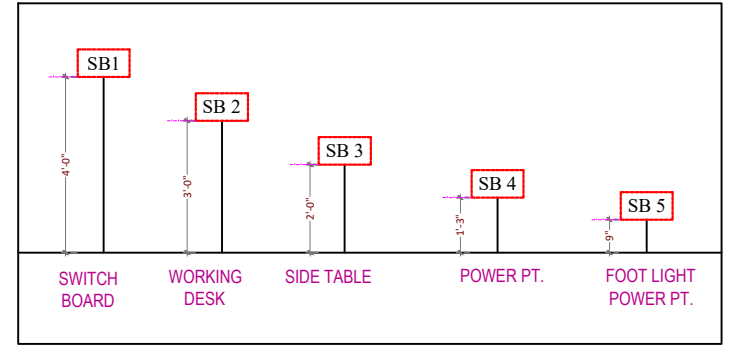

ELECTRICAL LEGEND		
SYMBOLS		
	CL	CEILING LIGHT POINT-18W
	CL	CEILING LIGHT POINT-12W
	SL	SURFACE MOUNTED CEILING LIGHT POINT
	WL	WALL LIGHT POINT @8'-0"
	SB	SWITCH BOARD
	P	6 AMP PLUG POINT
	PP	6/16 AMP PLUG POINT
	TV	TELEVISION POINT
	F	FAN
	F	FAN - TOILET
	WF	WALL MOUNT FAN
	EX	EXHAUST FAN
	S	SPEAKER POINT
	DB	DISTRIBUTION POINT
	TP	TELEPHONE POINT
	J	JUNCTION BOX
	WR	WIFI ROUTER
	C	CAMERA
	CE	CEILING EXHAUST
	RL01	1W LED BED SIDE ADJUSTABLE READING LIGHT WITH INBUILT SWITCH (RL)
	NC	NORMAL CONTROL
	TWC	TWO WAY CONTROL

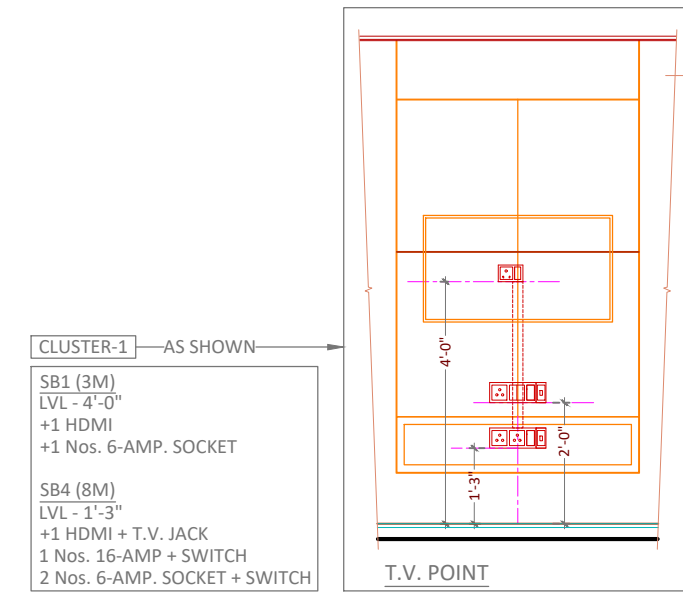

MASTER BEDROOM WALL ELECTRICAL PLAN