



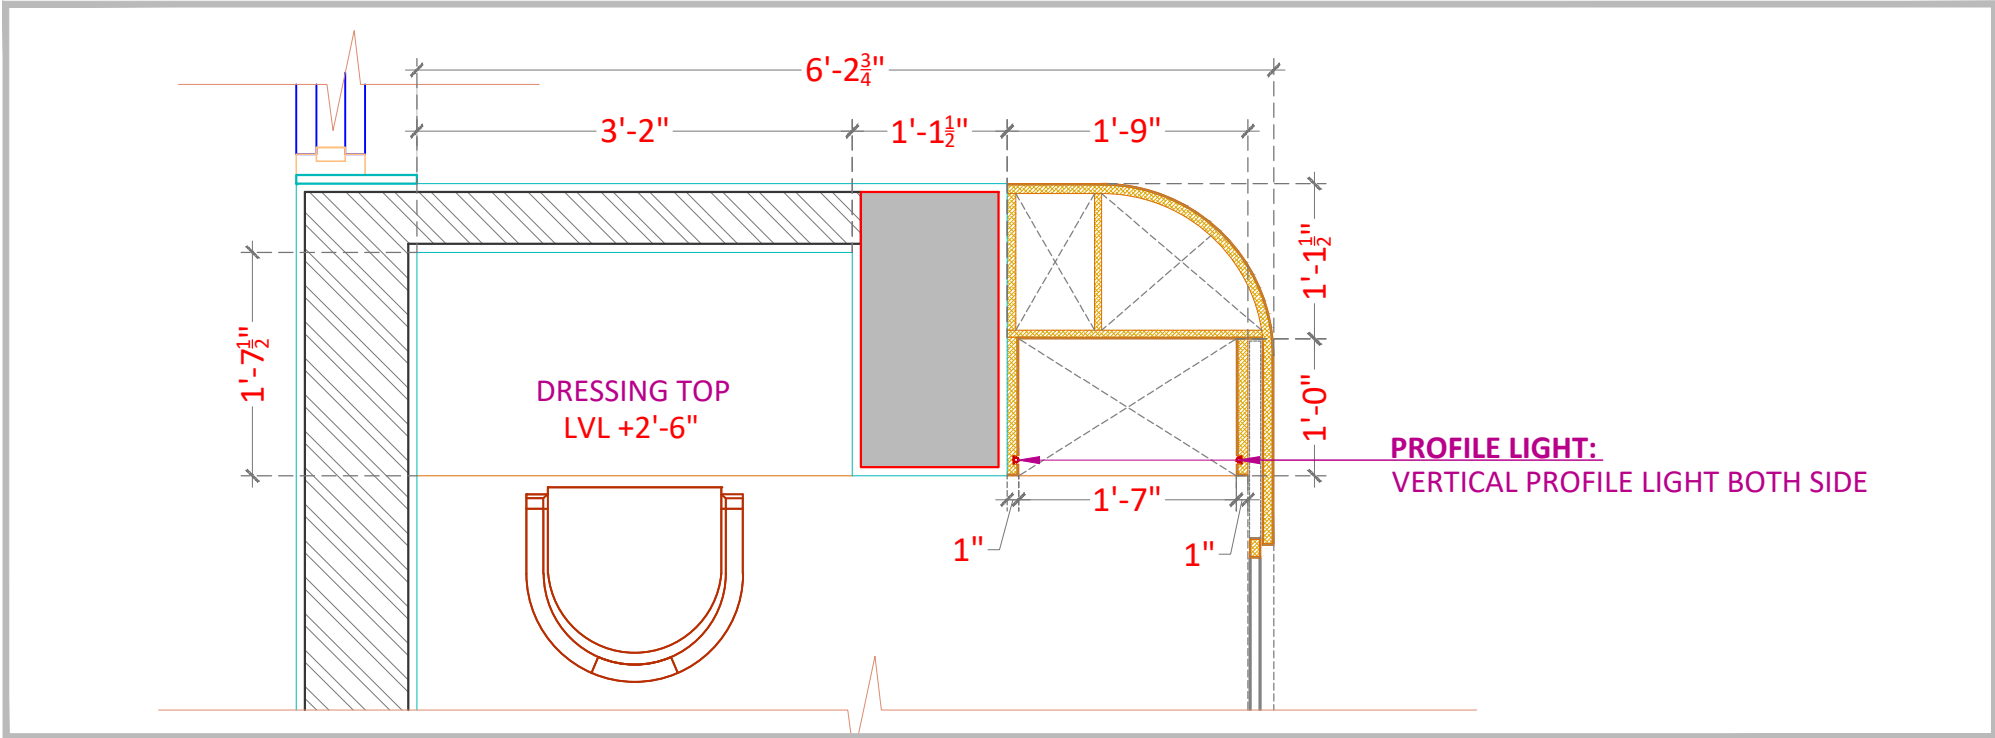

A) WORKING PLAN

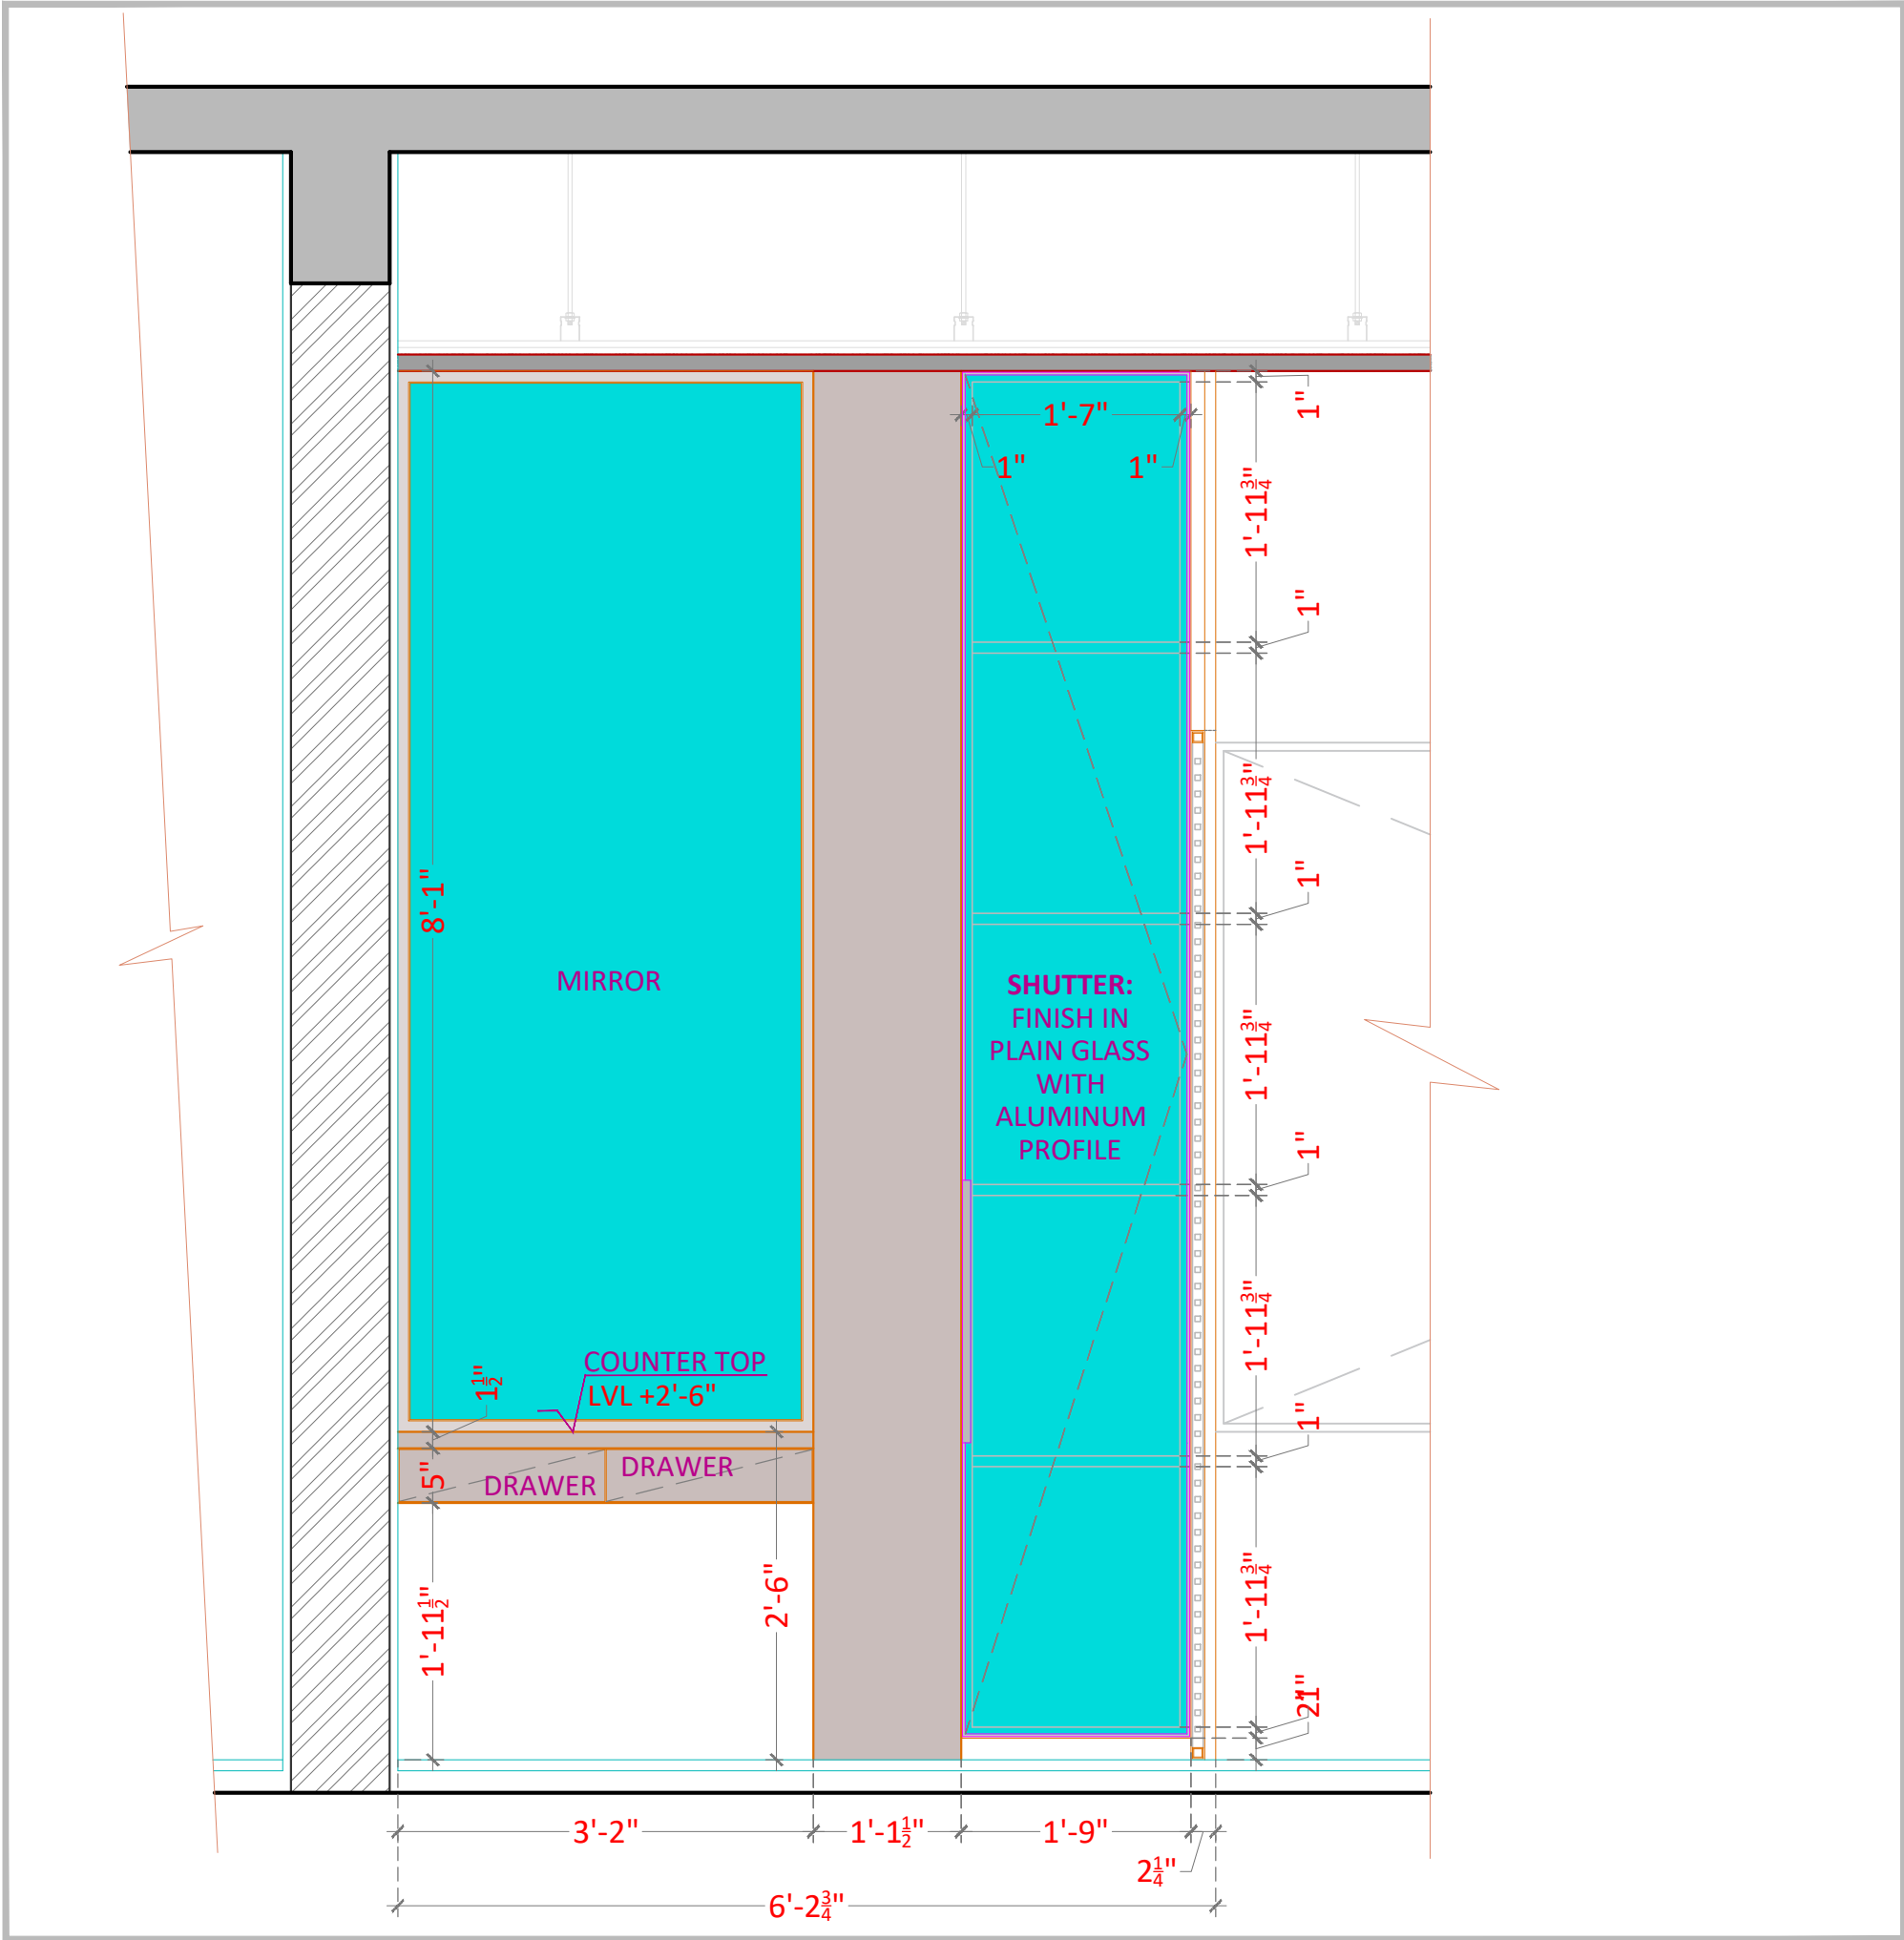

B) WORKING ELEVATION

DRESSING UNIT DETAIL