



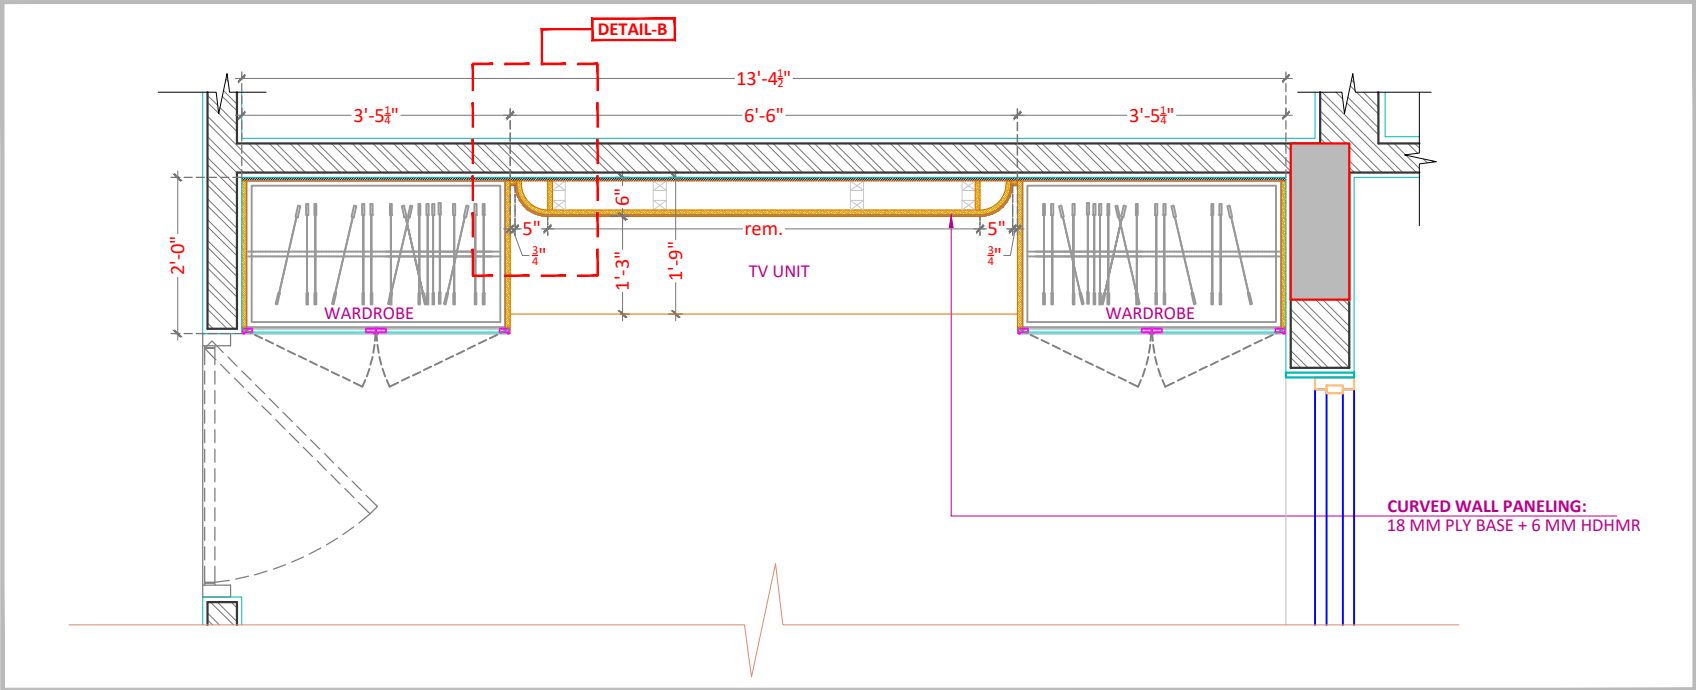


A)PART WORKING PLAN




C)REFERENCE IMAGE

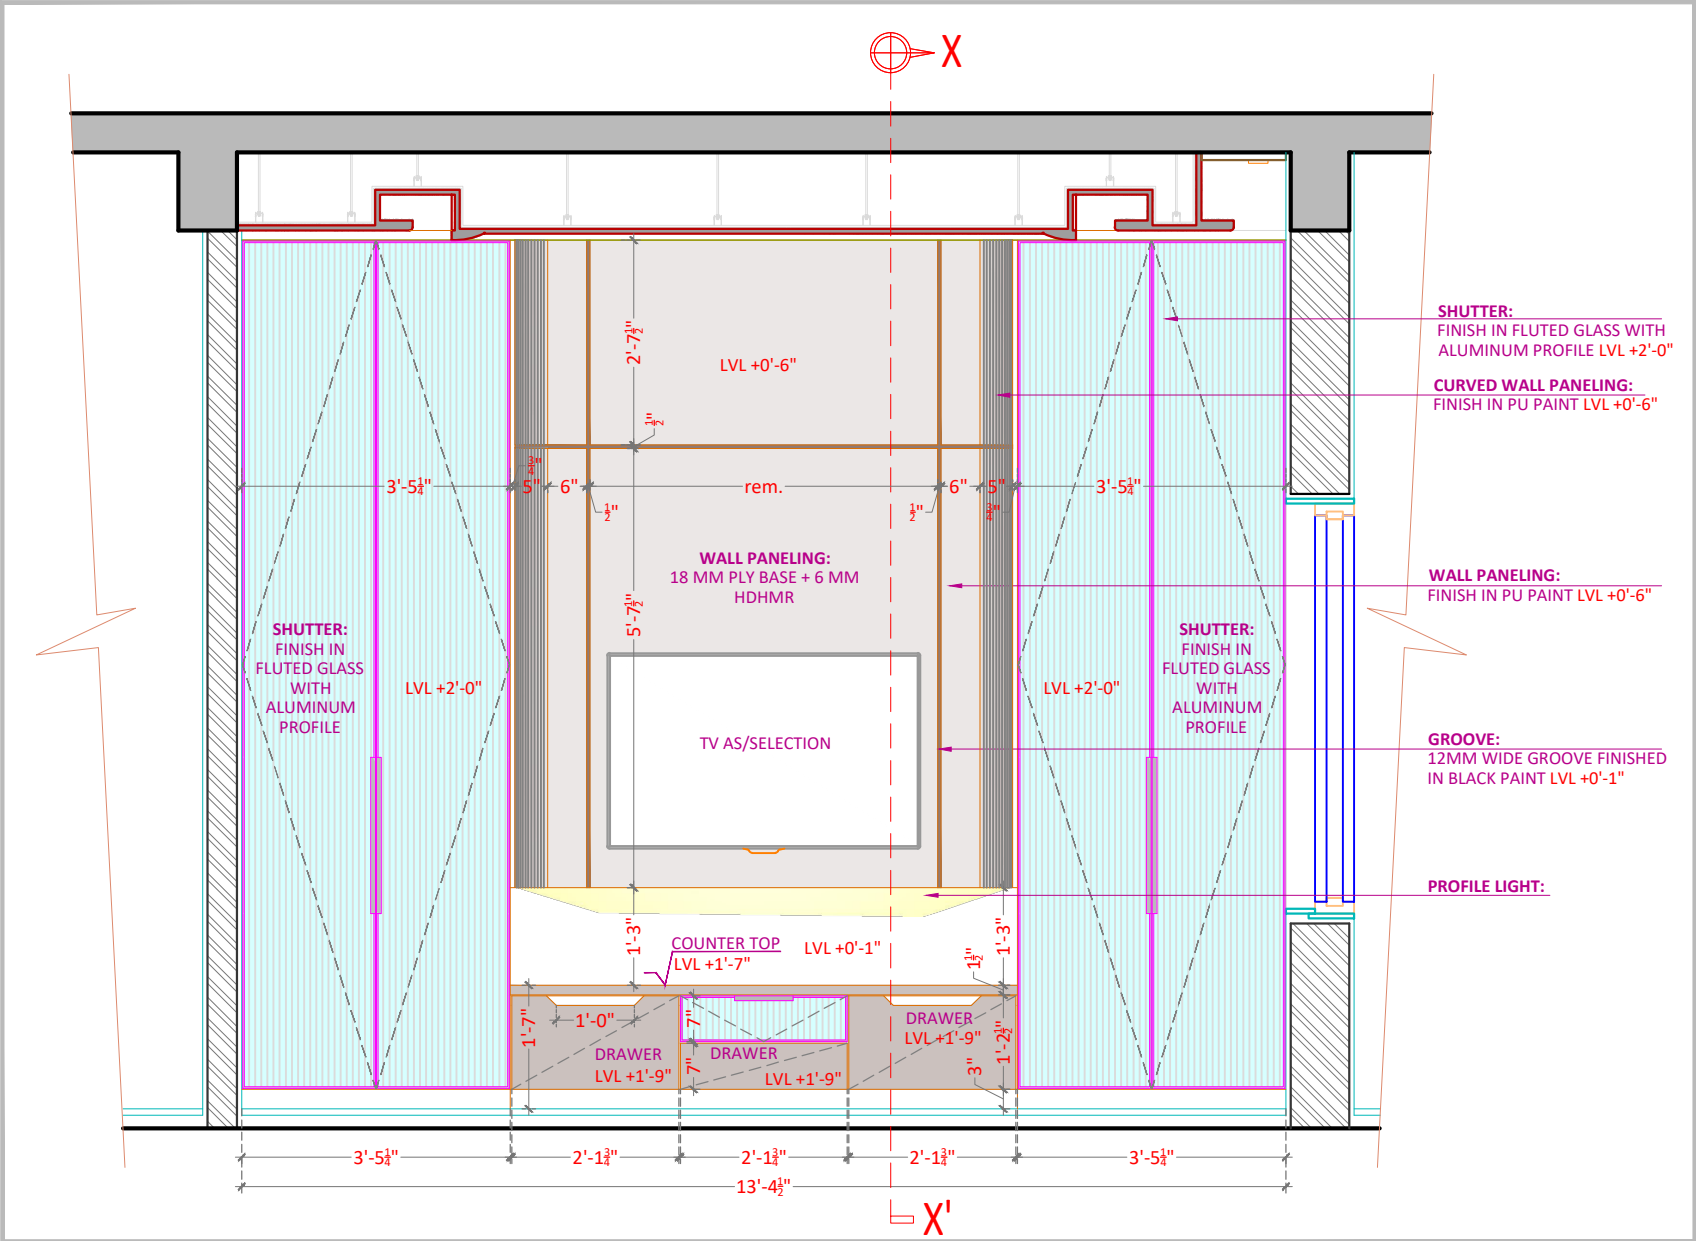


B)WORKING ELEVATION

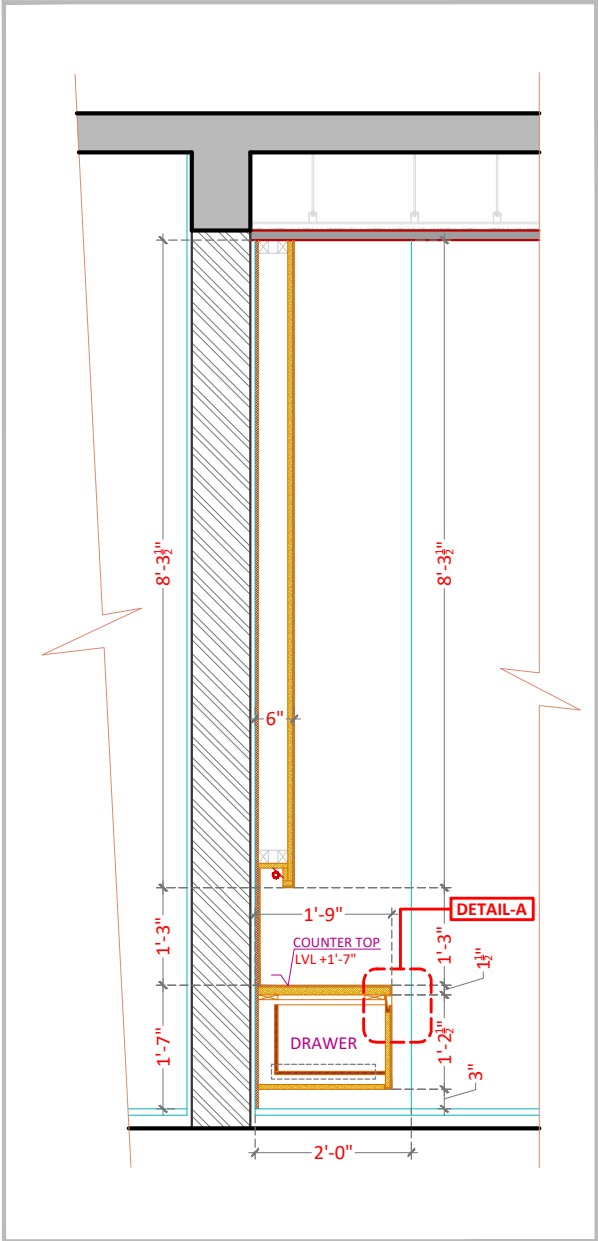

D)SECTION X - X'

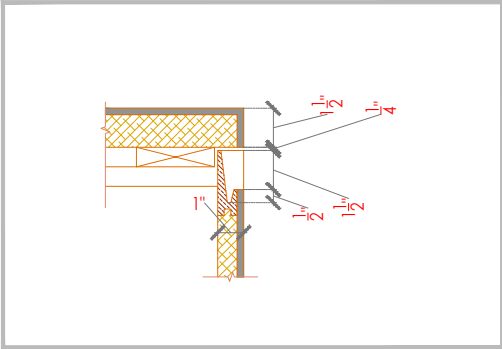

E)DETAIL - A

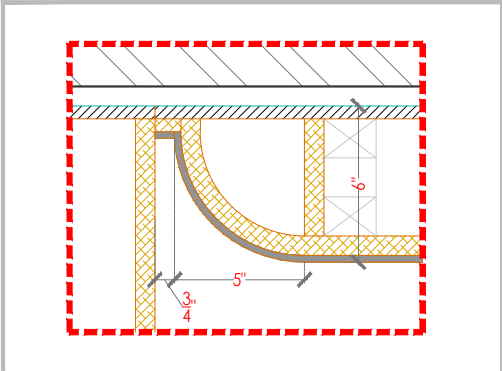

F)DETAIL - B